



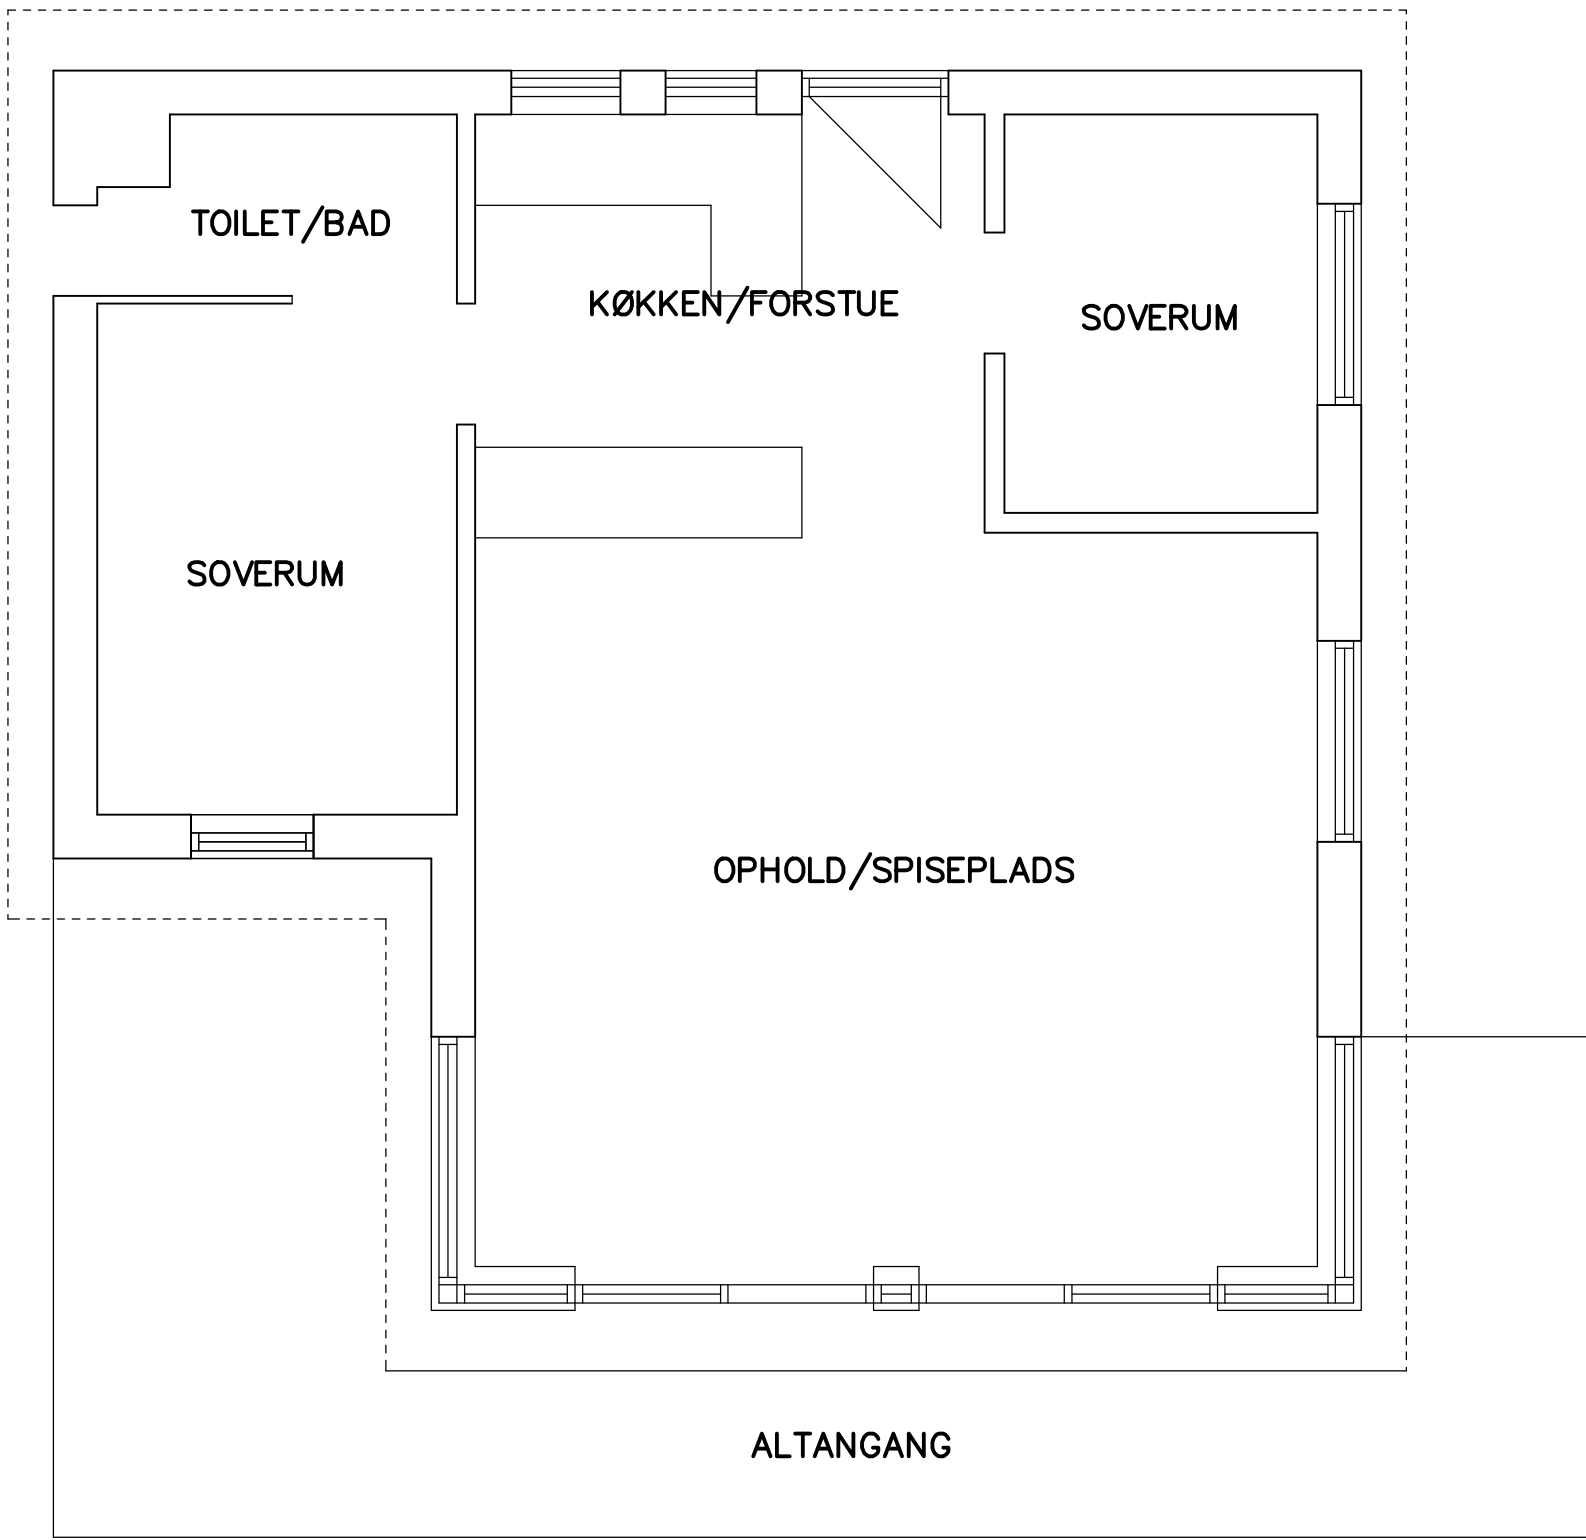

OPMPLINGSPLAN AF STUEETAGEN MÅL 1:50

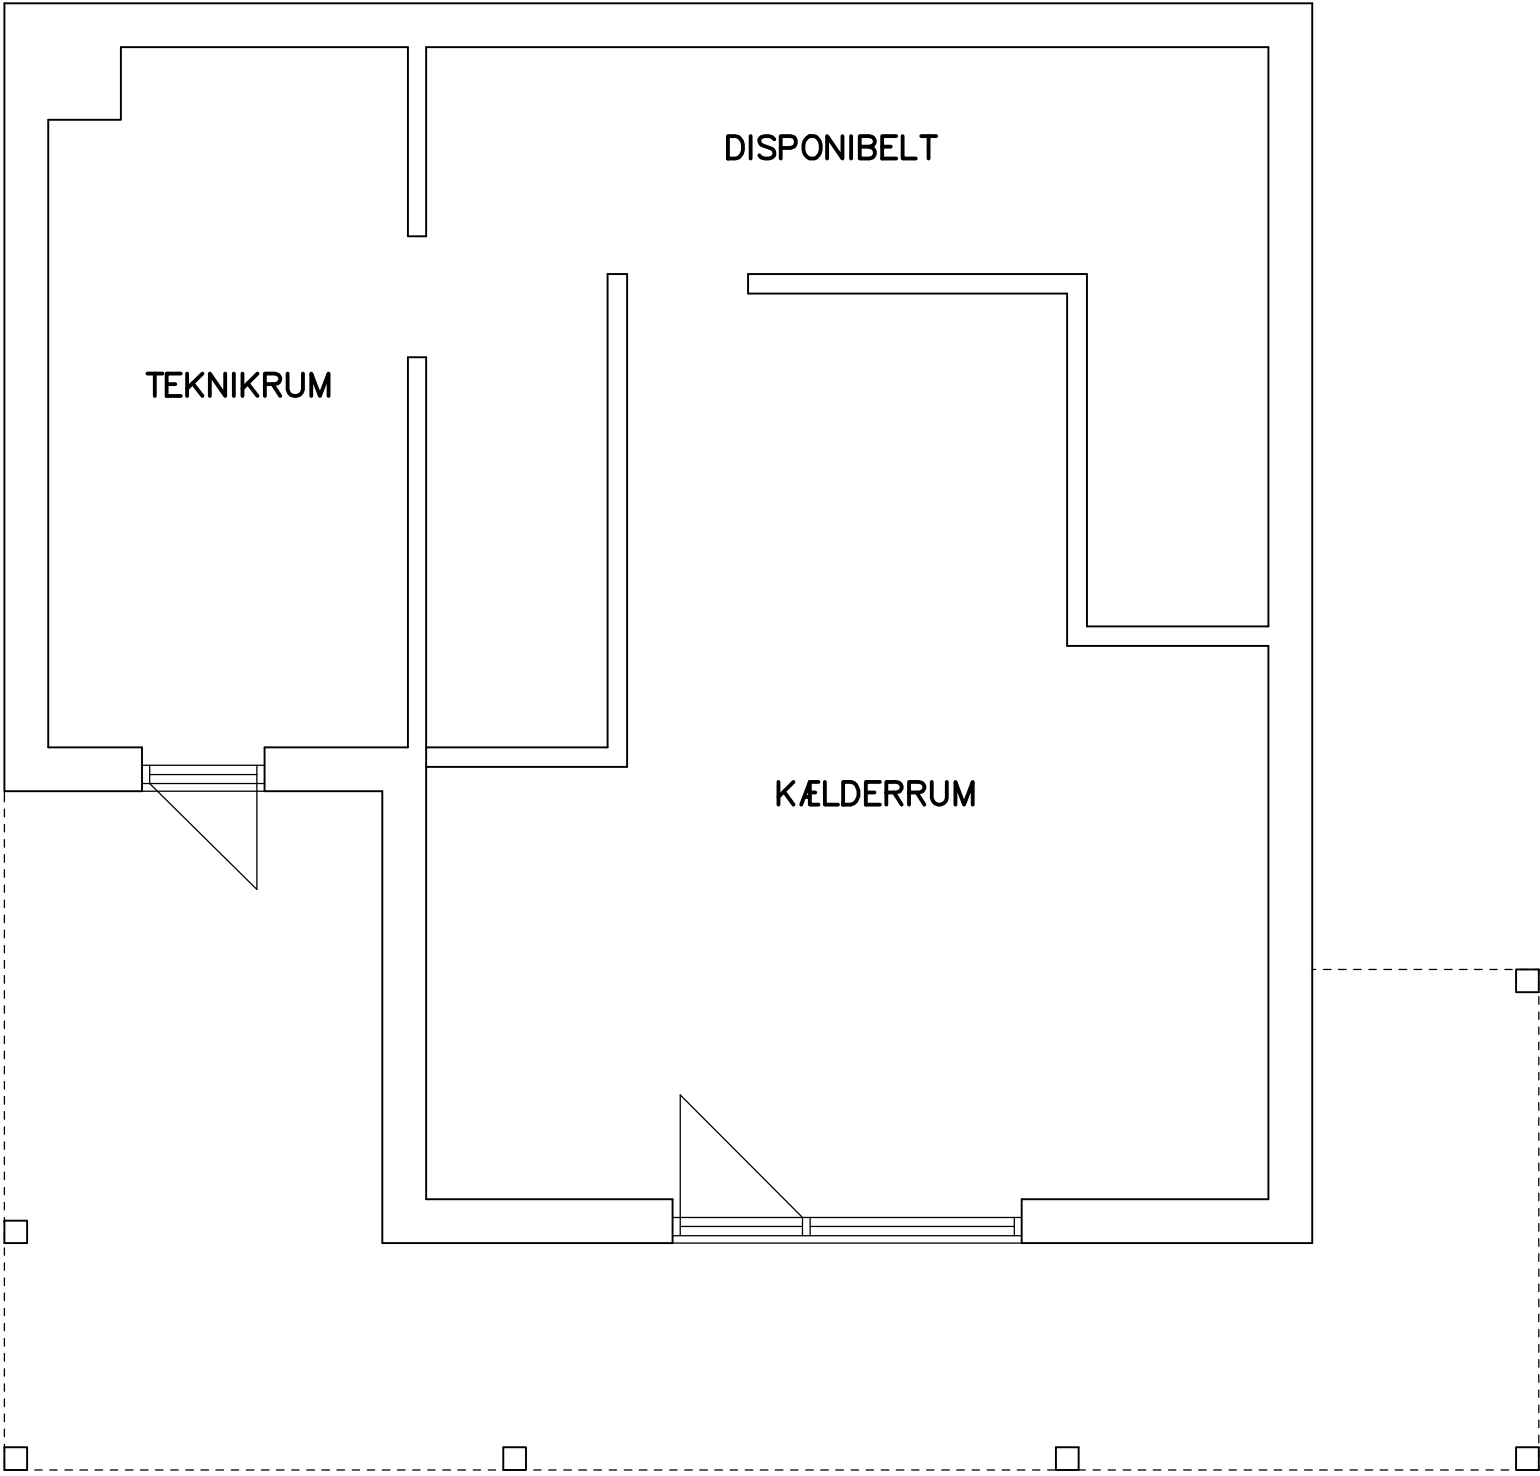

OPMÅLINGSPLAN AF KÆLDER MÅL 1:50

MYNDIGHEDSPROJEKT

BODIL OG HENNING HEISELBERG
OM OG TILBYGNING AF SOMMERHUS GRØNHØJ STRANDVEJ 168, GRØNHØJ

EMNE: OPMÅLINGSPLAN AF STUEETAGEN OG KÆLDER

DATO: 27.03.2026

MÅL: 1:50


SAGSNR.: 25/426

TEGN. NR.:

10

Arkitekttegnestuen Yderskov ApS

Danserhøj 38
9700 Brønderslev
Tlf. 29723427

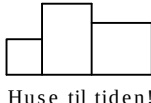

Huse til tiden!