




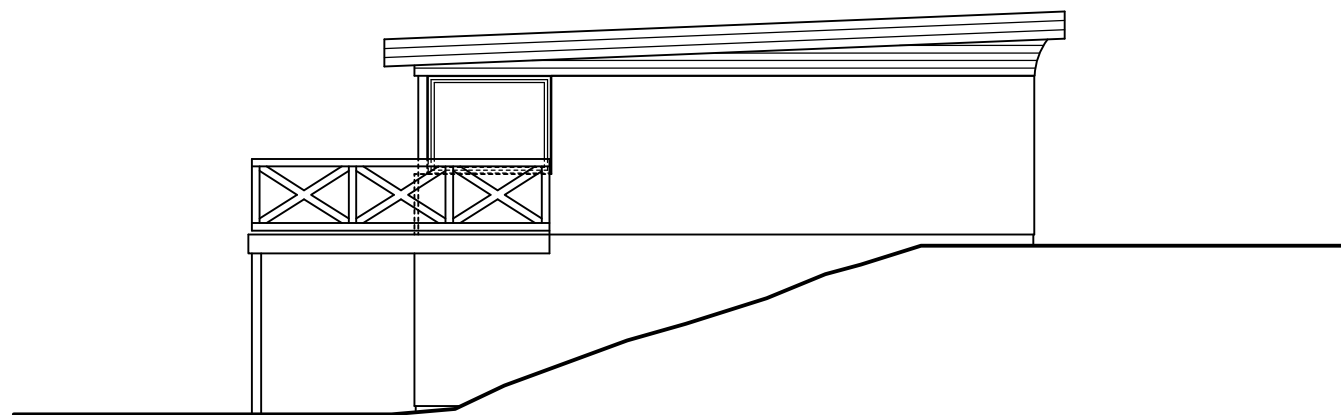


OPMÅLINGSGAVL MOD SYD MÅL 1:100

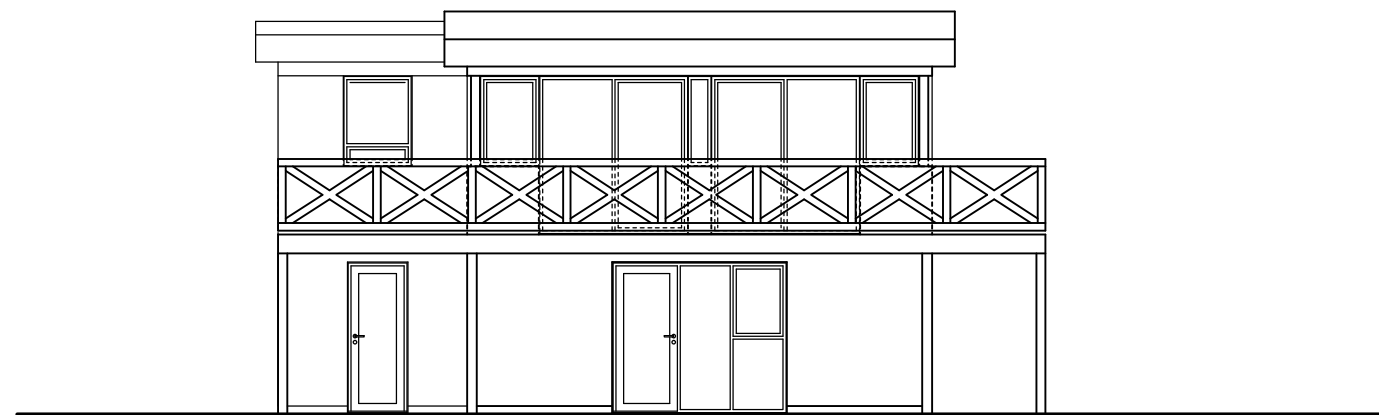

OPMÅLINGSFACADE MOD VEST MÅL 1:100

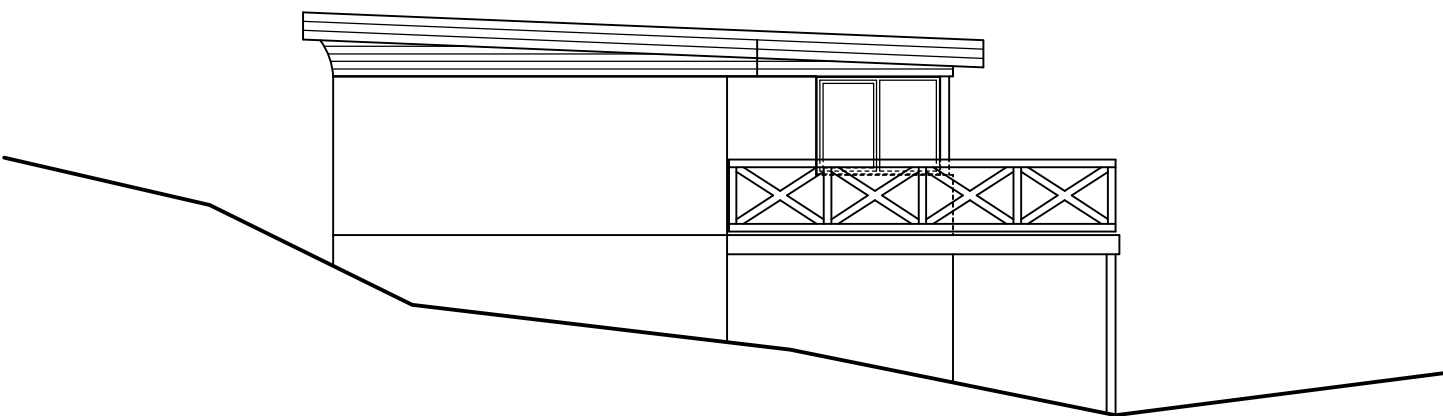

OPMÅLINGSGAVL MOD NORD MÅL 1:100

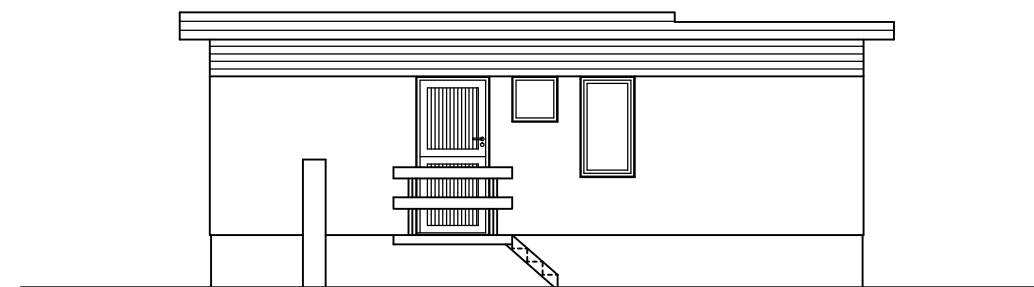

OPMÅLINGSFACADE MOD ØST MÅL 1:100

MYNDIGHEDSPROJEKT

**BODIL OG HENNING HEISELBERG
OM OG TILBYGNING AF SOMMERHUS GRØNHØJ STRANDVEJ 168, GRØNHØJ**

EMNE: OPMÅLINGSFACADER

DATO: 27.03.2026

MÅL: 1:100


SAGSNR.: 25/426

TEGN. NR.:

11

Arkitekttegnestuen Yderskov ApS

Danserhøj 38
9700 Brønderslev
Tlf. 29723427

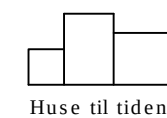

Huse til tiden!