



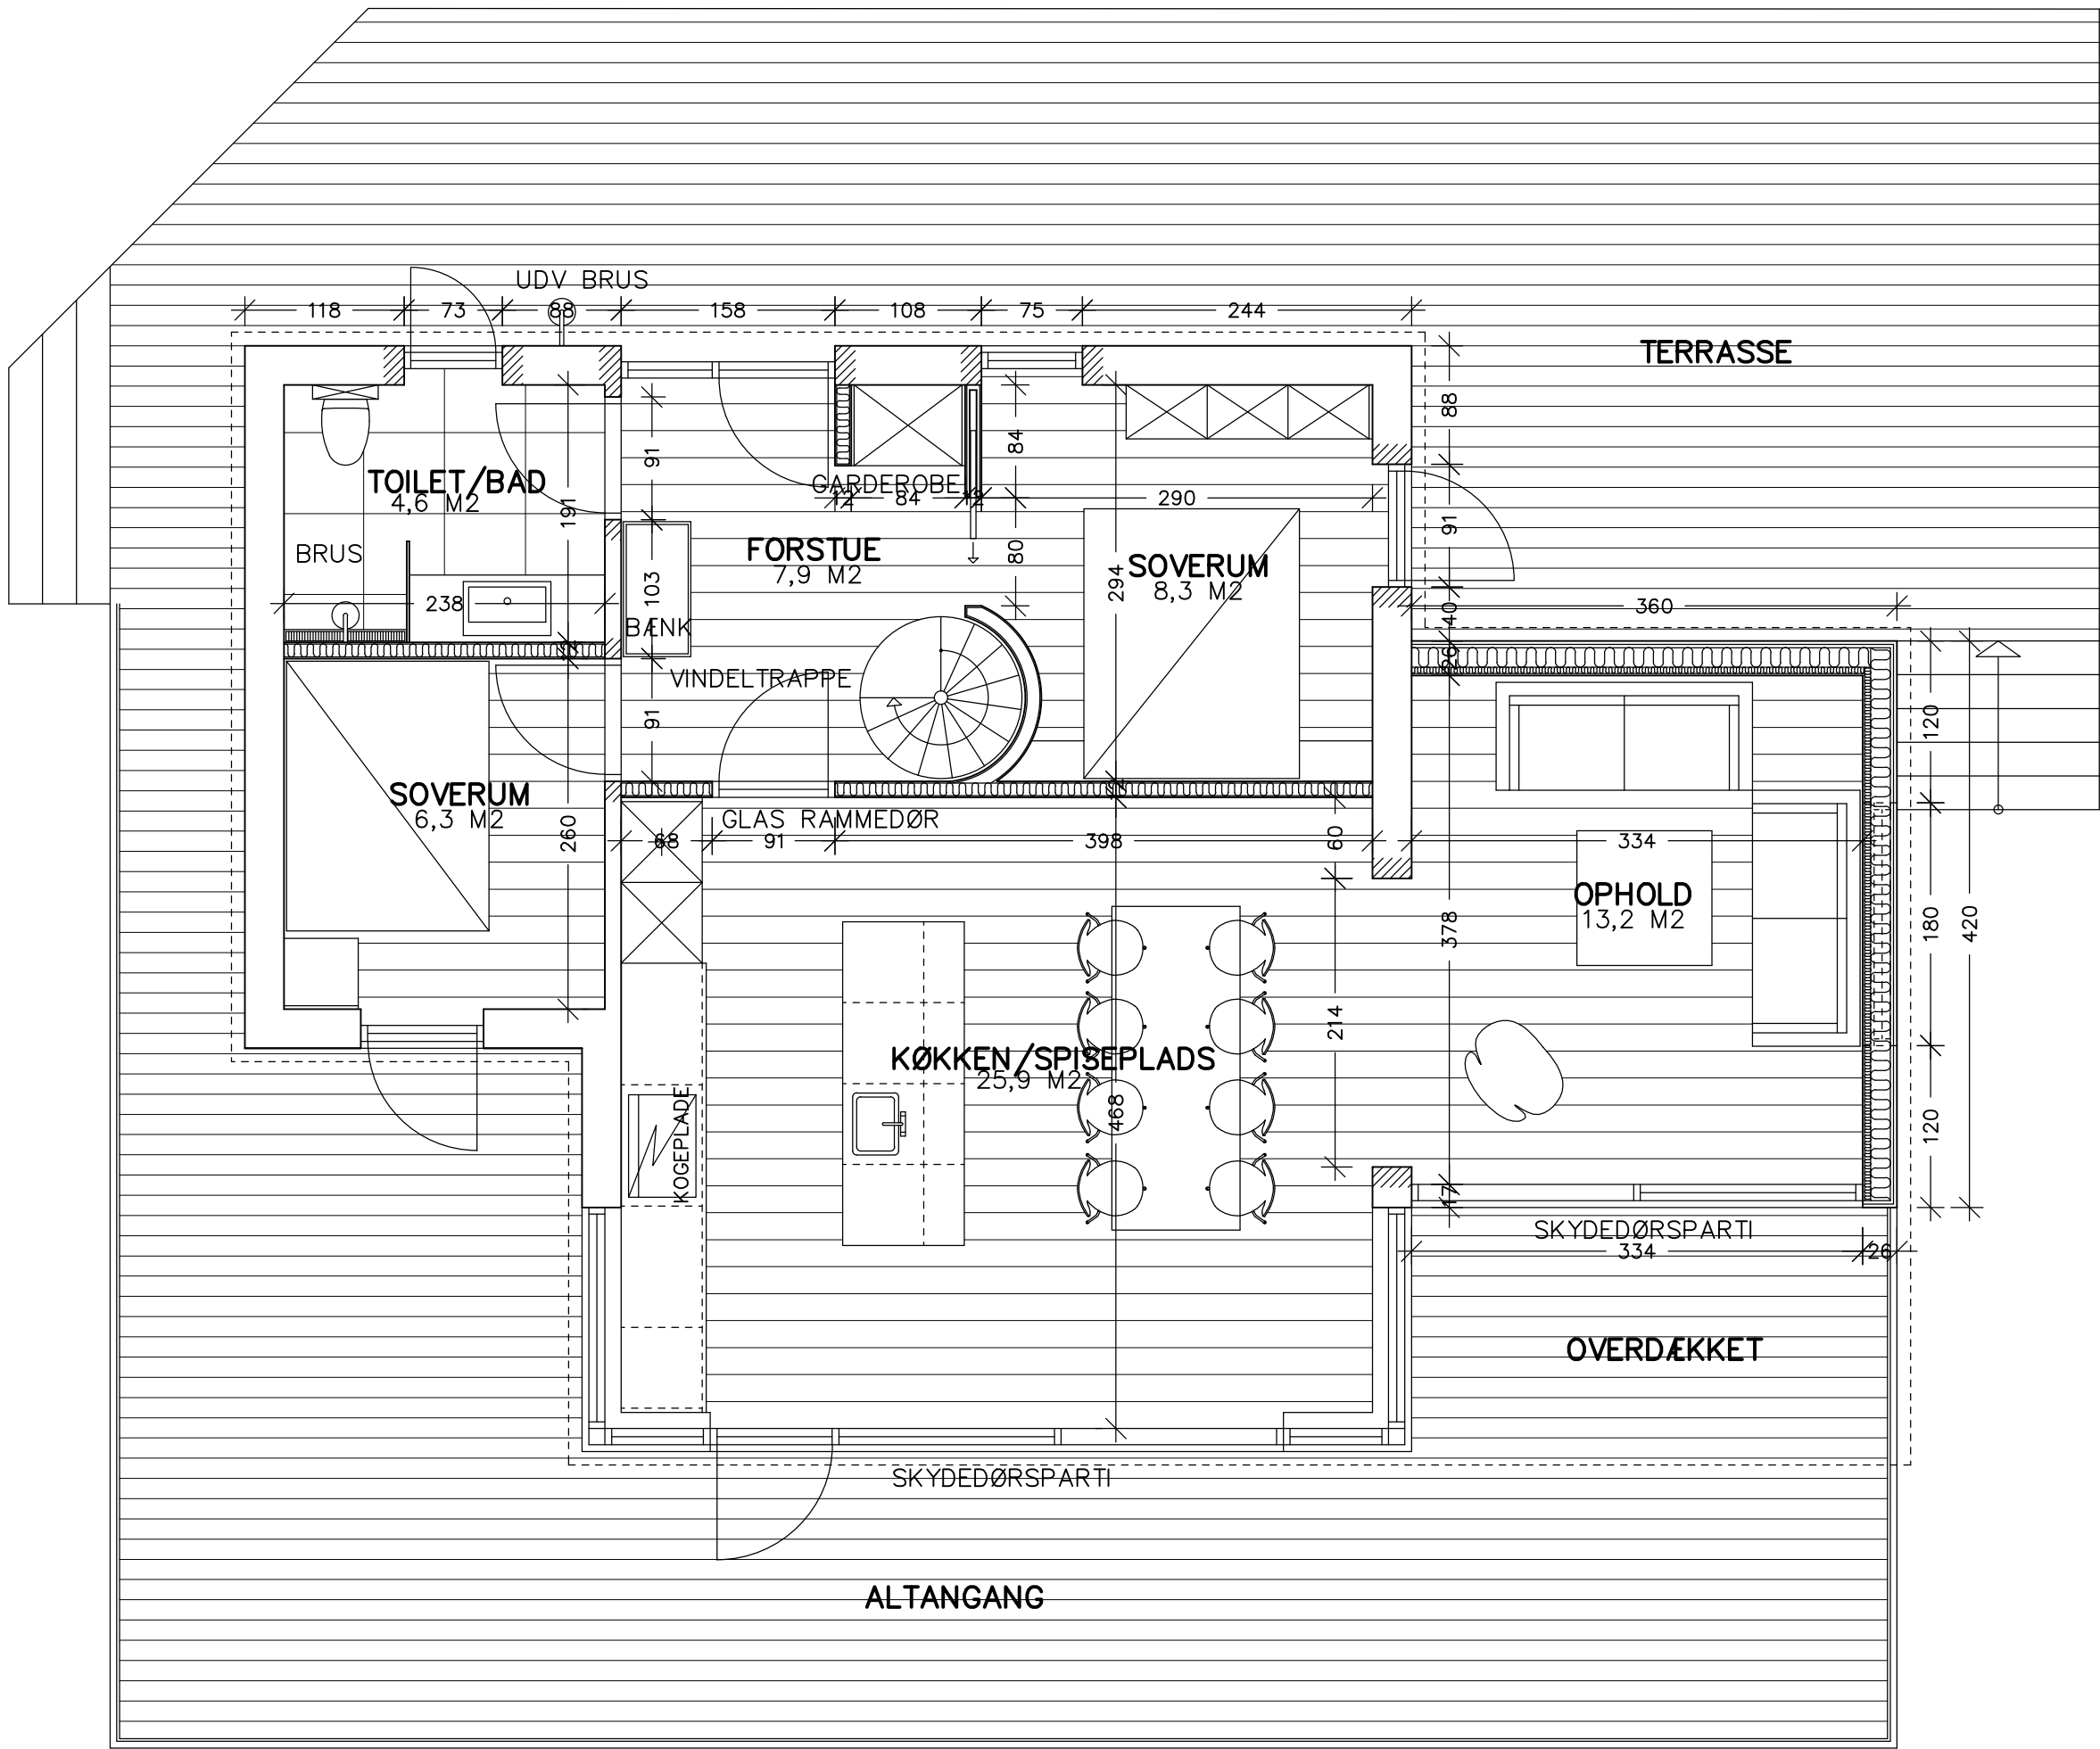

STUEPLAN MÅL 1: 500

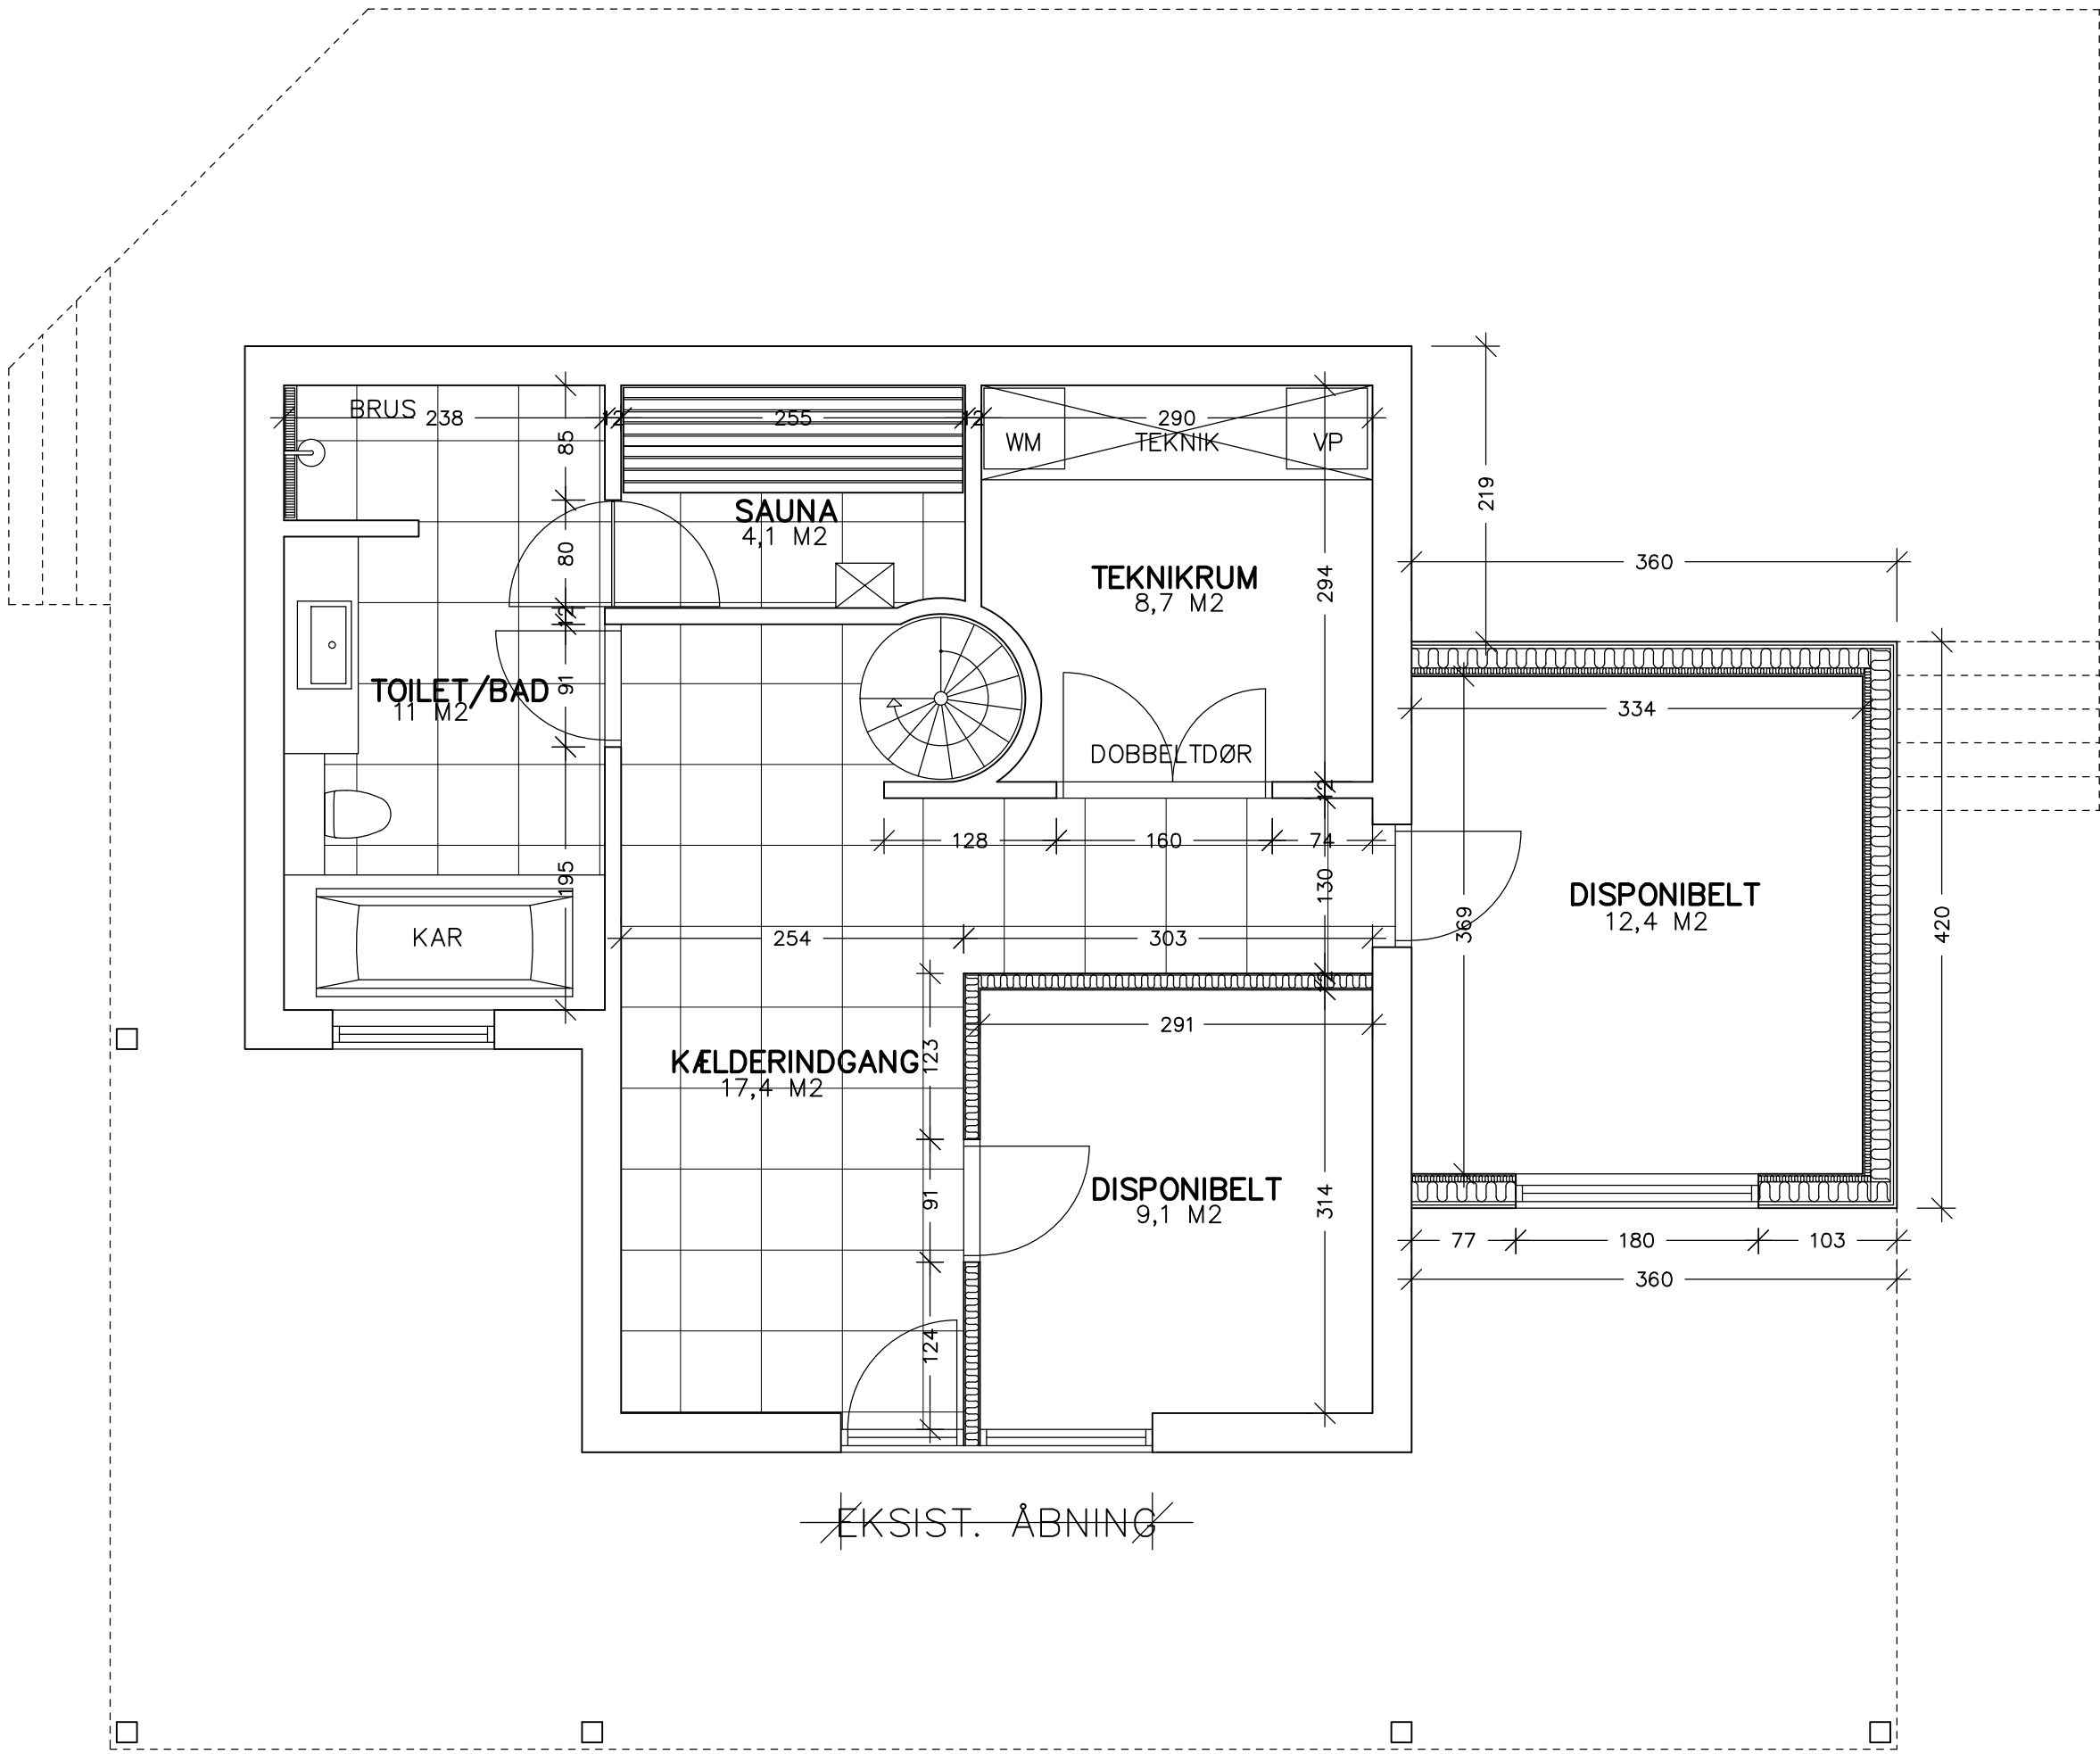

KÆLDERPLAN MÅL 1: 500

MYNDIGHEDSPROJEKT

BODIL OG HENNING HEISELBERG
OM OG TILBYGNING AF SOMMERHUS GRØNHØJ STRANDVEJ 168, GRØNHØJ

EMNE: FREMTIDIG STUE OG KÆLDERPLAN

DATO: 27.03.2026

MÅL: 1:50


SAGSNR.: 25/426

TEGN. NR.:

20

Arkitekttegnestuen Yderskov ApS

Danserhøj 38
9700 Brønderslev
Tlf. 29723427

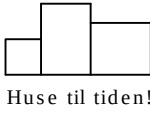

Huse til tiden!