
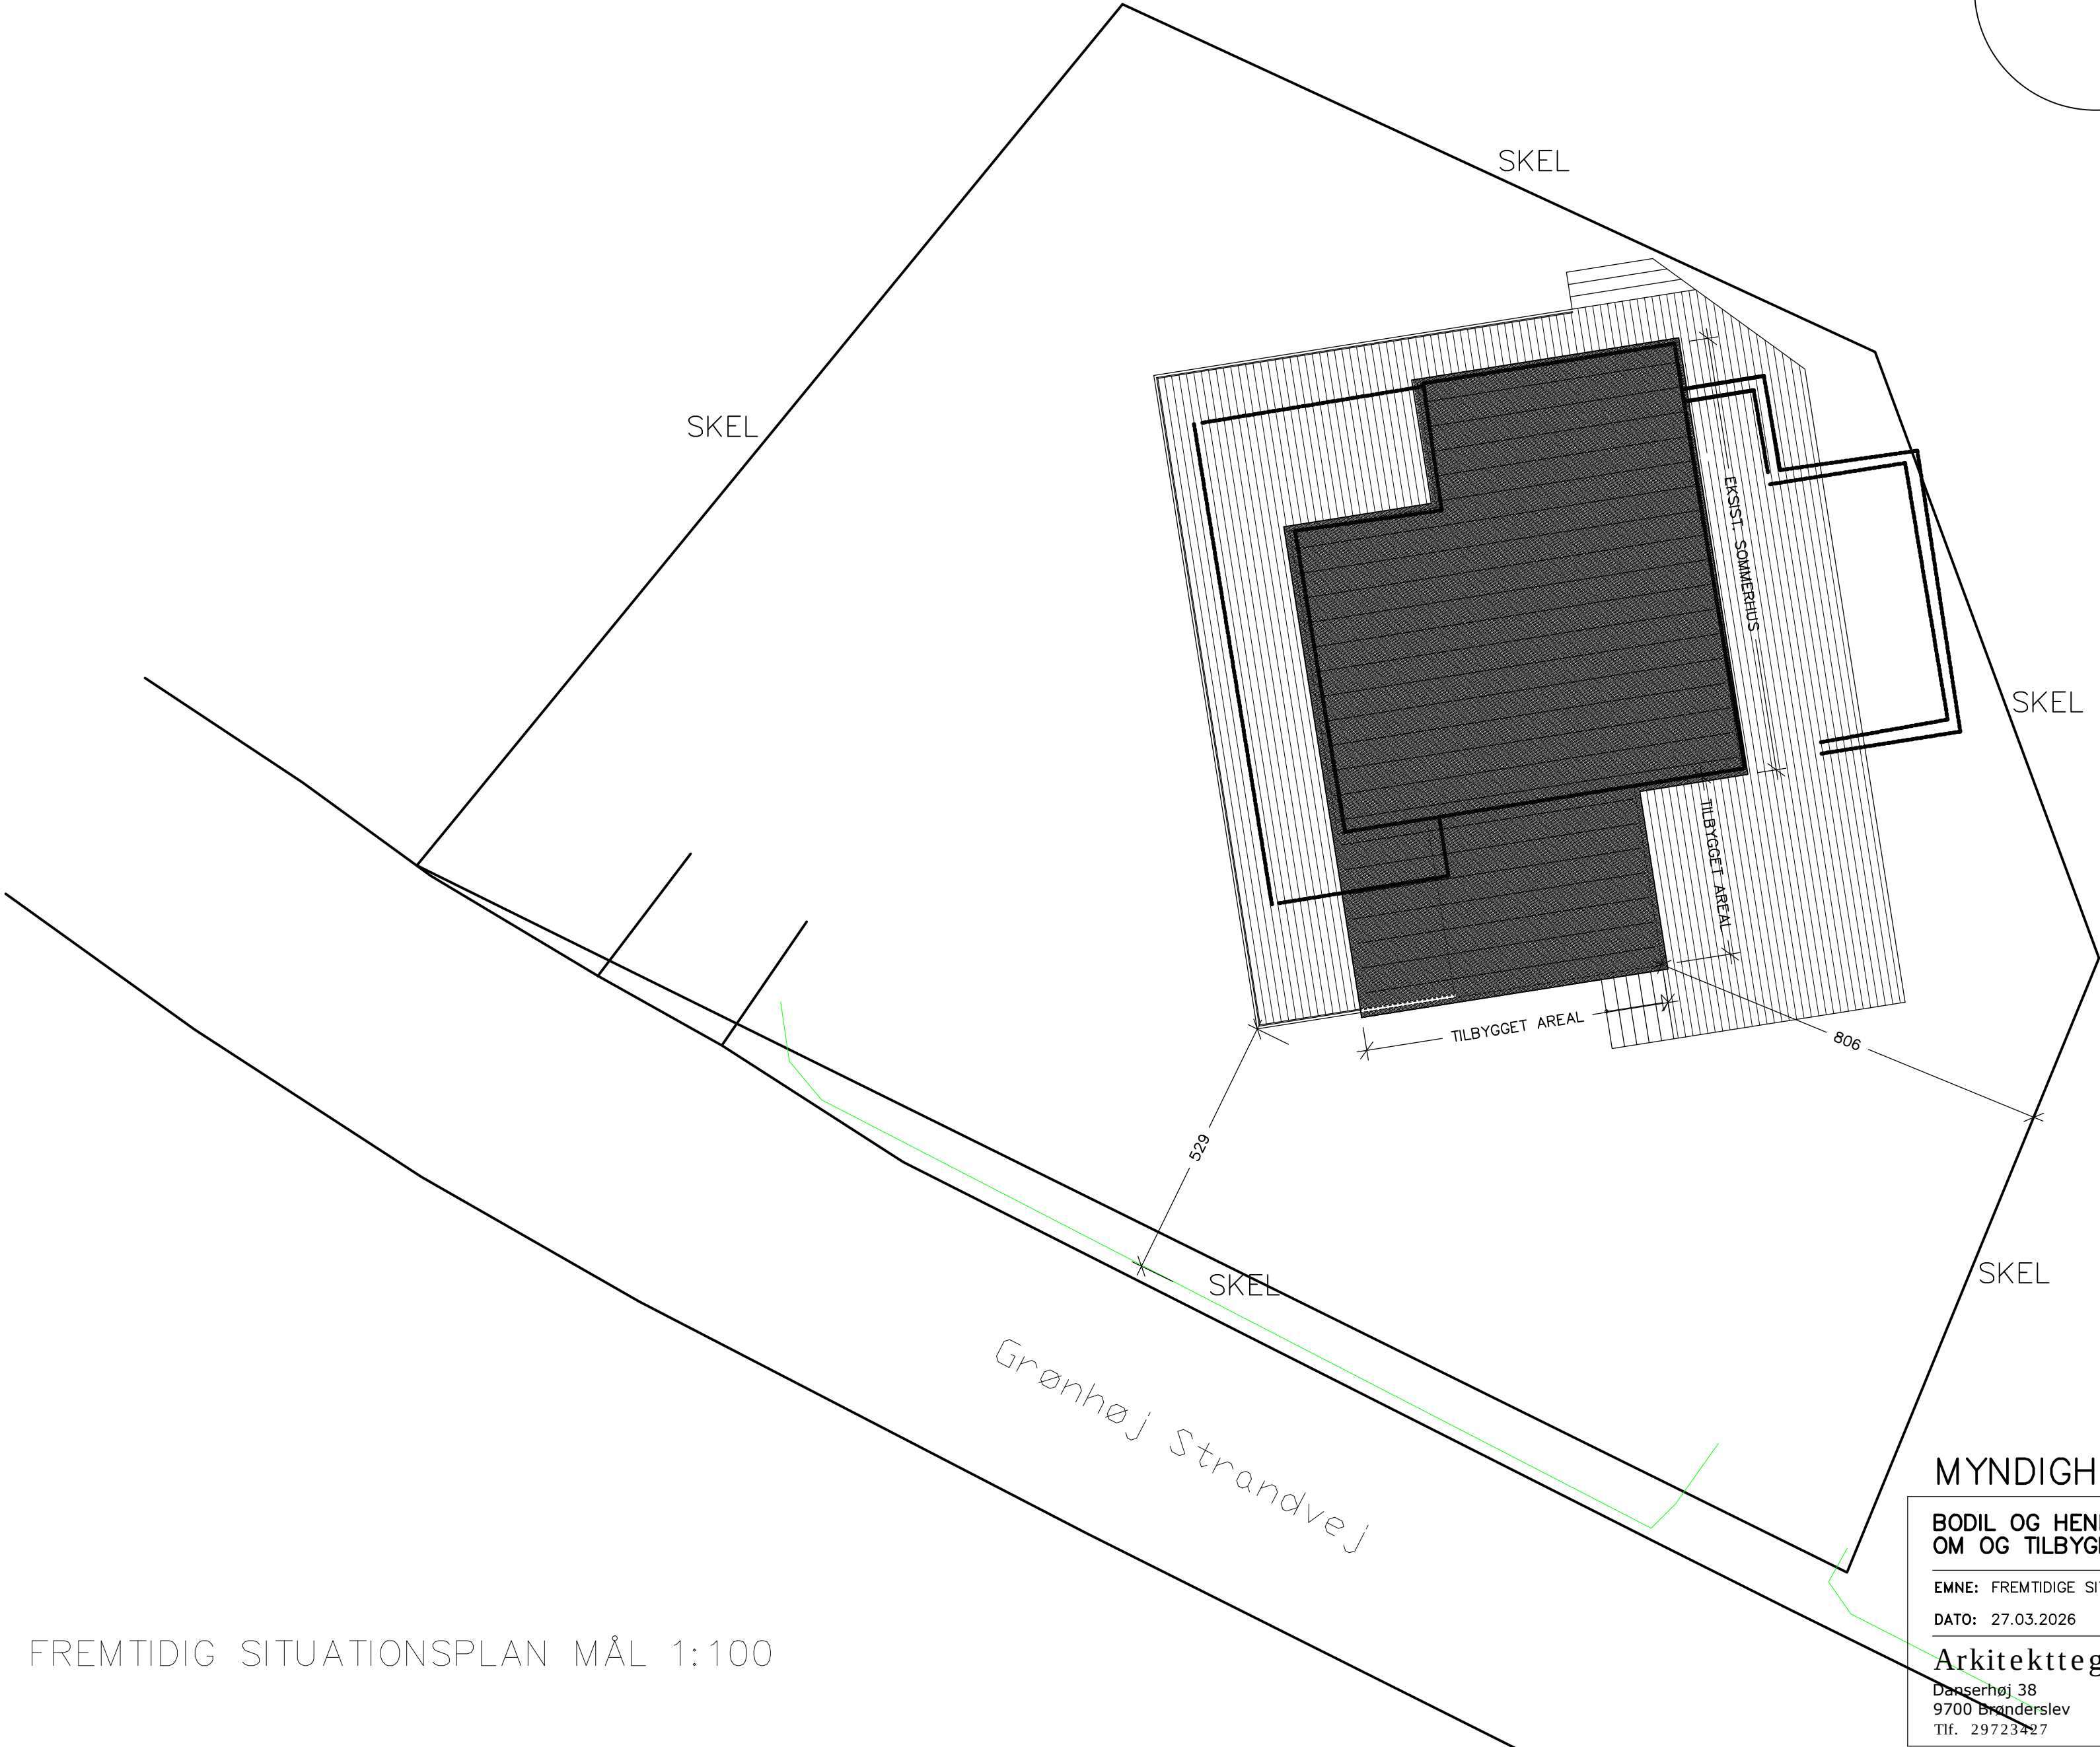


SAMLET GRUNDAREAL	615 M2
EKSIST. BEBYGGET AREAL FOR BEBOELSE	63 M2
TILBEBYGGET AREAL FOR BEBOELSE	15 M2
KÆLDER HERAF 5 M2 TIL SAUNA	78 M2
OVERDÆKKET AREAL	7 M2
SAMLET AREAL FOR BEREGNING AF BEBYG.%	83 M2
BEBYG.%	13,5 %

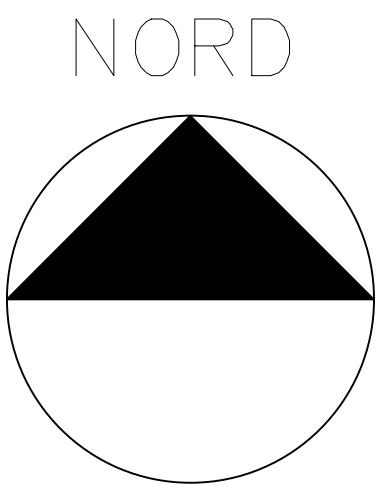

FREMTIDIG SITUATIONSPLAN MÅL 1:100

MYNDIGHEDSPROJEKT

BODIL OG HENNING HEISELBERG
OM OG TILBYGNING AF SOMMERHUS GRØNHØJ STRANDVEJ 168, GRØNHØJ

EMNE: FREMTIDIGE SITUATIONSPLAN
DATO: 27.03.2026 MÅL: 1:100 SAGSNR.: 25/426 TEGN. NR.: 90

Arkitekttegnestuen Yderskov ApS
Dønsenhøj 38
9700 Brønderslev
Tlf. 29723427

Huse til tiden!