


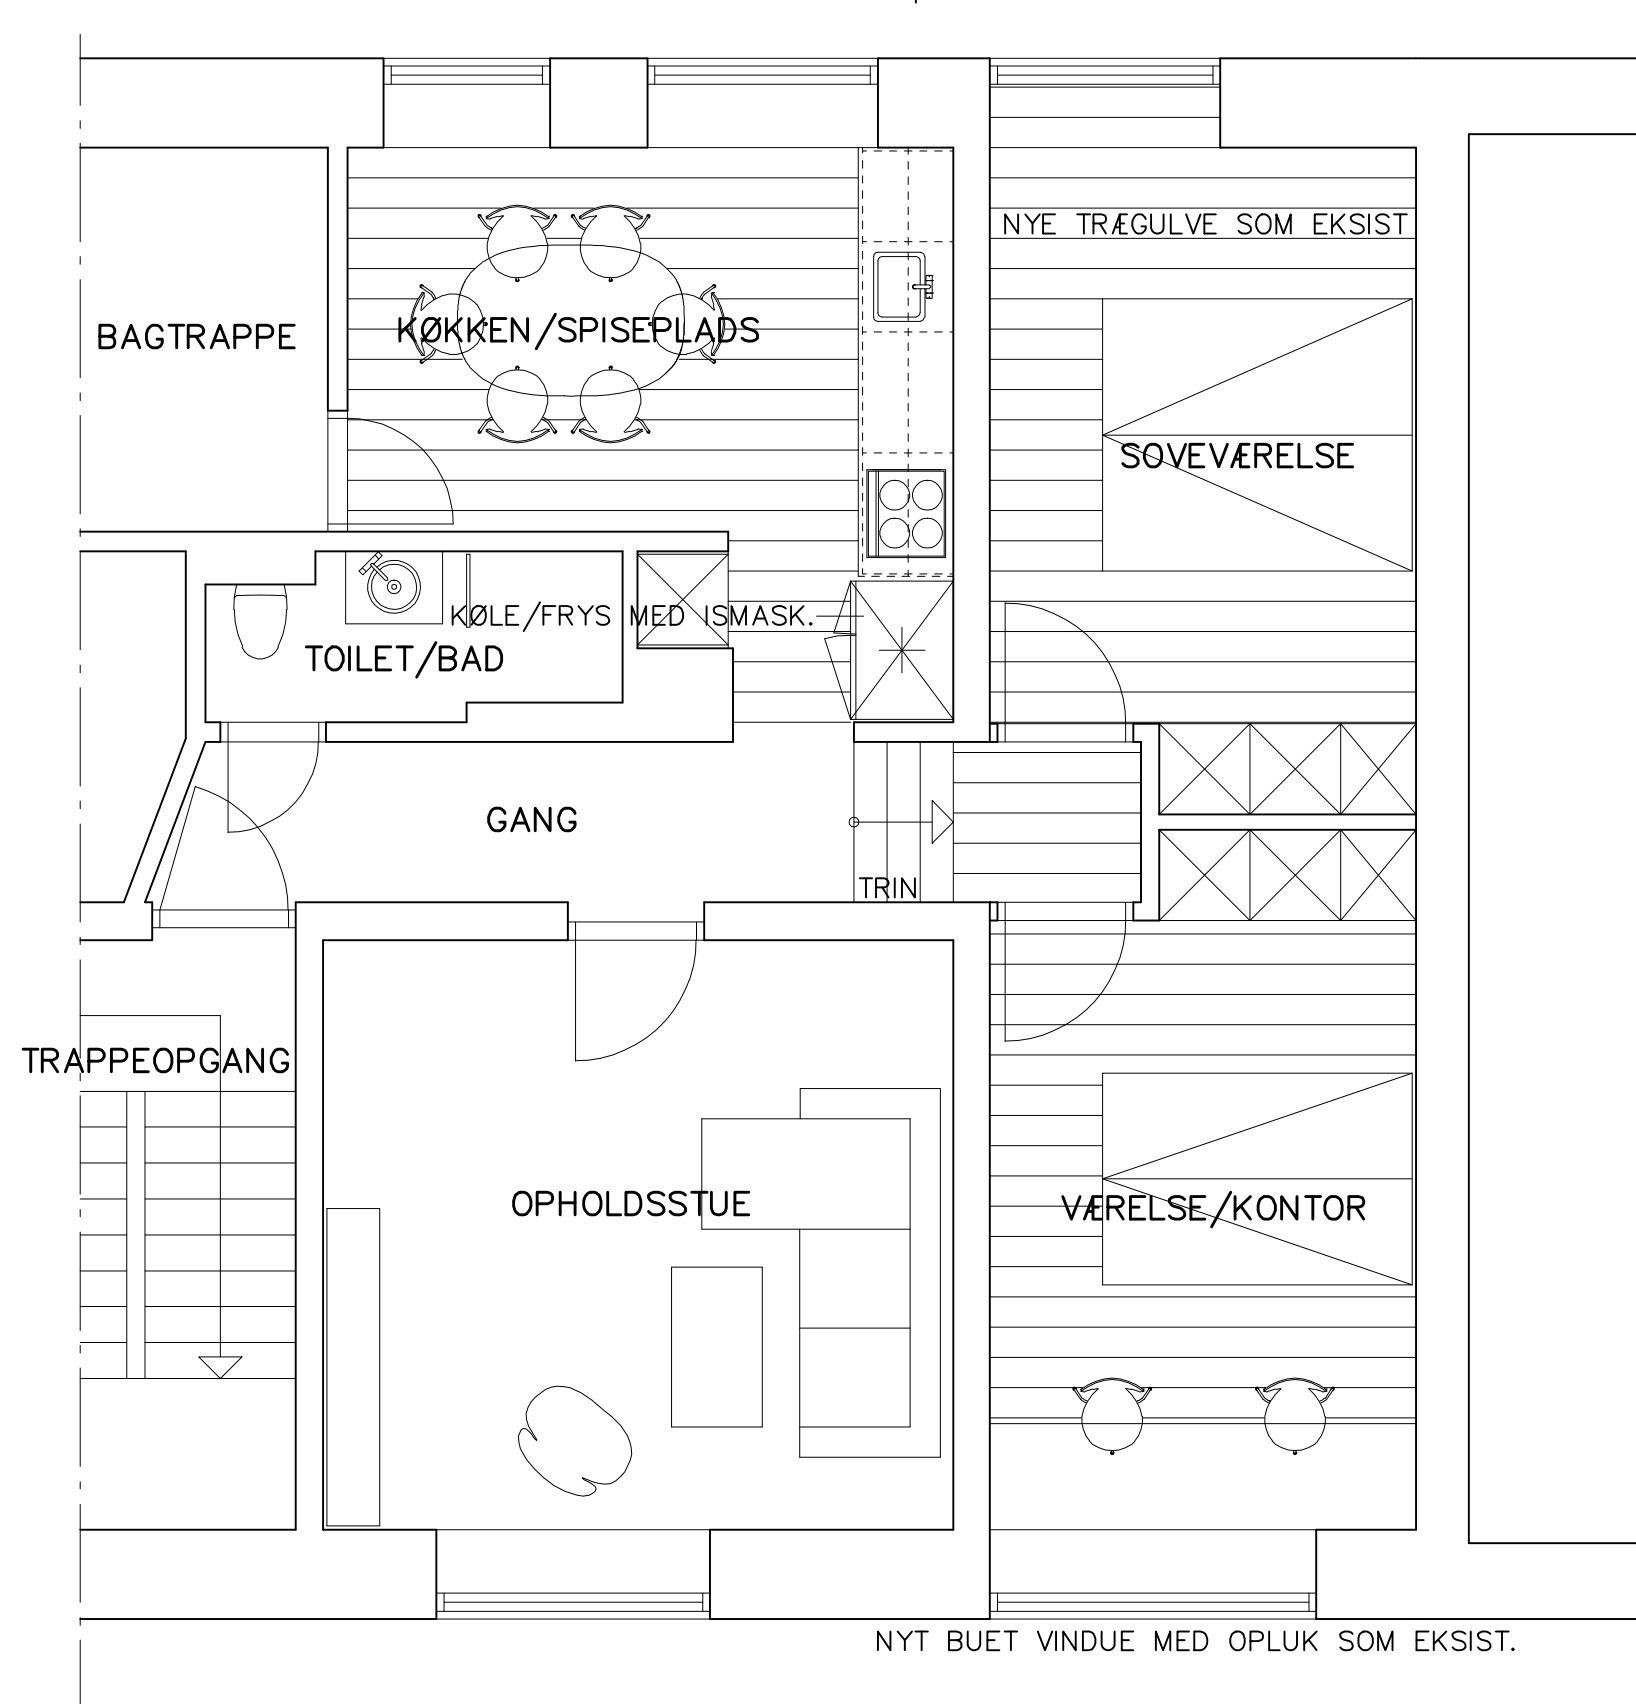

FREMTIDIG PLAN MÅL 1:50

MYNDIGHEDSPROJEKT

LOTTE SOFIE KAAE OG CHRIS YDESKOV
OM-TILBYGNING AF LEJLIGHED, ÅGADE 25 1TH, AALBORG

EMNE: FREMTIDIGE PLANER

DATO: 06.01.2018

MÅL: 1:50

SAGSNR.: -/-

TEGN. NR.:

20

Arkitekttegnestuen Yderskov ApS

Danserhøj 38
9700 Brønderslev
Tlf. 98811217/29723427

